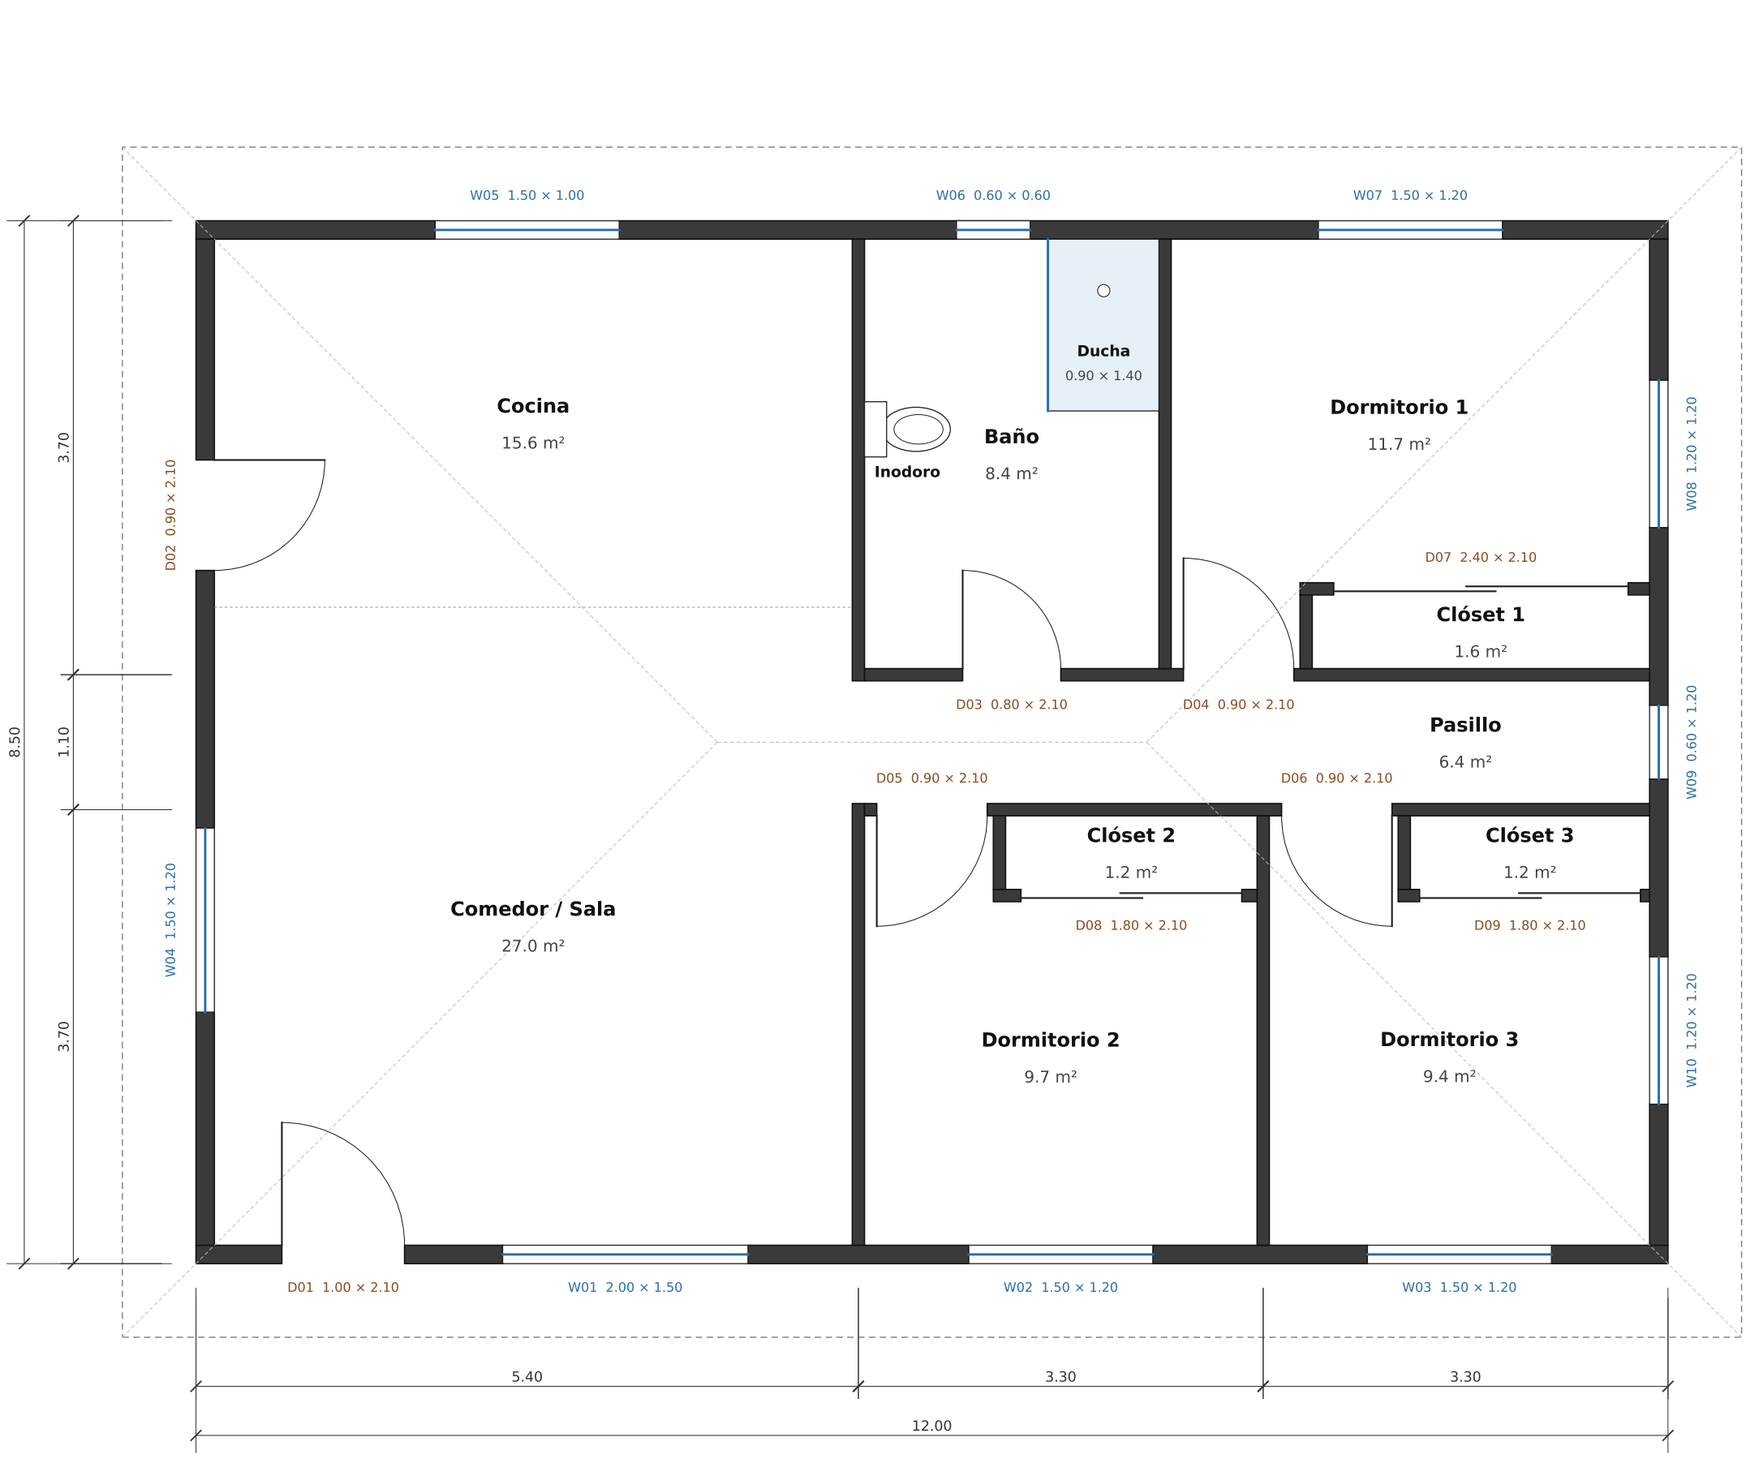

Casa de tres dormitorios

Planta arquitectónica

Escala 1:50 (hoja A3)

Cotas en metros; vanos: ancho × alto

Área interior 92.3 m²

Área de construcción 102.0 m²

Línea discontinua: techo

Creado por Sebastian

Cuadro de puertas y ventanas (m)

Marca	Ancho	Alto	Antepecho
W01	2.00	1.50	0.60
W02	1.50	1.20	0.90
W03	1.50	1.20	0.90
W04	1.50	1.20	0.90
W05	1.50	1.00	1.10
W06	0.60	0.60	1.60
W07	1.50	1.20	0.90
W08	1.20	1.20	0.90
W09	0.60	1.20	0.90
W10	1.20	1.20	0.90
D01	1.00	2.10	–
D02	0.90	2.10	–
D03	0.80	2.10	–
D04	0.90	2.10	–
D05	0.90	2.10	–
D06	0.90	2.10	–
D07	2.40	2.10	–
D08	1.80	2.10	–
D09	1.80	2.10	–