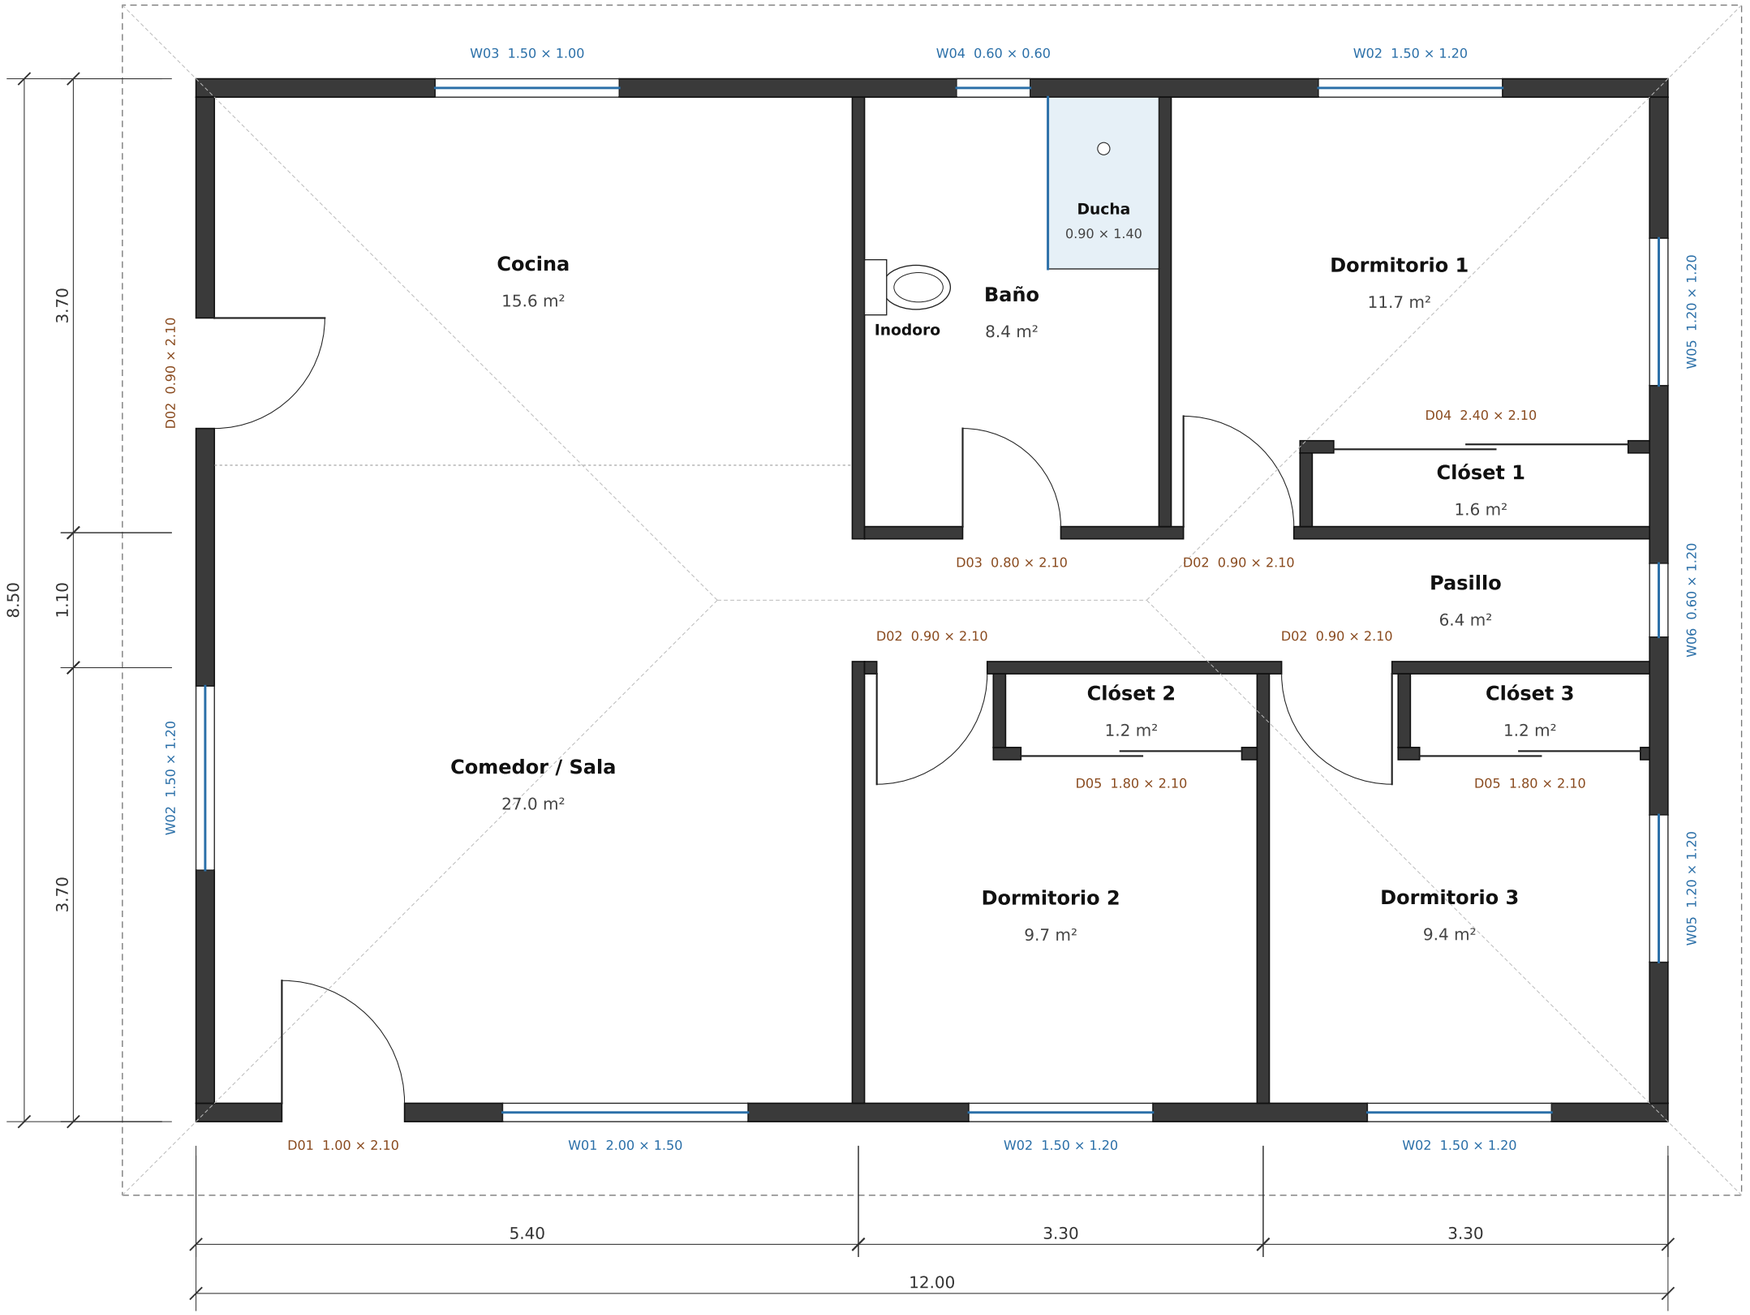

Casa de tres dormitorios

Planta arquitectónica

Escala 1:50 (hoja A3)

Cotas en metros; vanos: ancho × alto

Área interior 92.3 m²

Área de construcción 102.0 m²

Línea discontinua: techo

Creado por Sebastian Mudarra

Hoja 1 de 3

Cuadro de puertas y ventanas (m)

Marca	Cant.	Ancho	Alto	Antepecho
W01	1	2.00	1.50	0.60
W02	4	1.50	1.20	0.90
W03	1	1.50	1.00	1.10
W04	1	0.60	0.60	1.60
W05	2	1.20	1.20	0.90
W06	1	0.60	1.20	0.90
D01	1	1.00	2.10	–
D02	4	0.90	2.10	–
D03	1	0.80	2.10	–
D04	1	2.40	2.10	–
D05	2	1.80	2.10	–

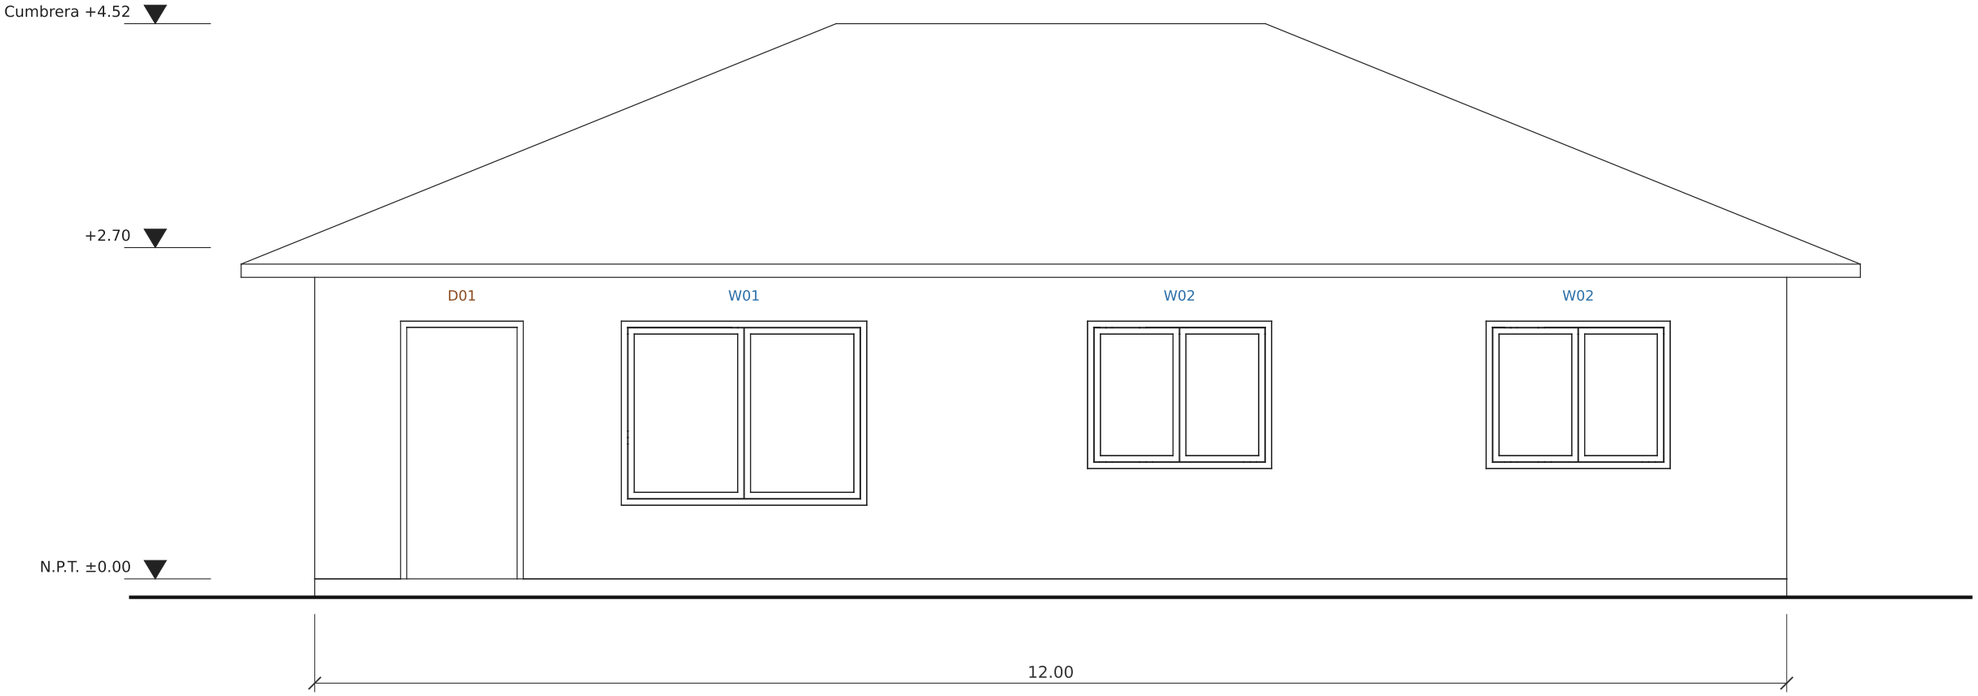

Fachada Sur

Escala 1:50

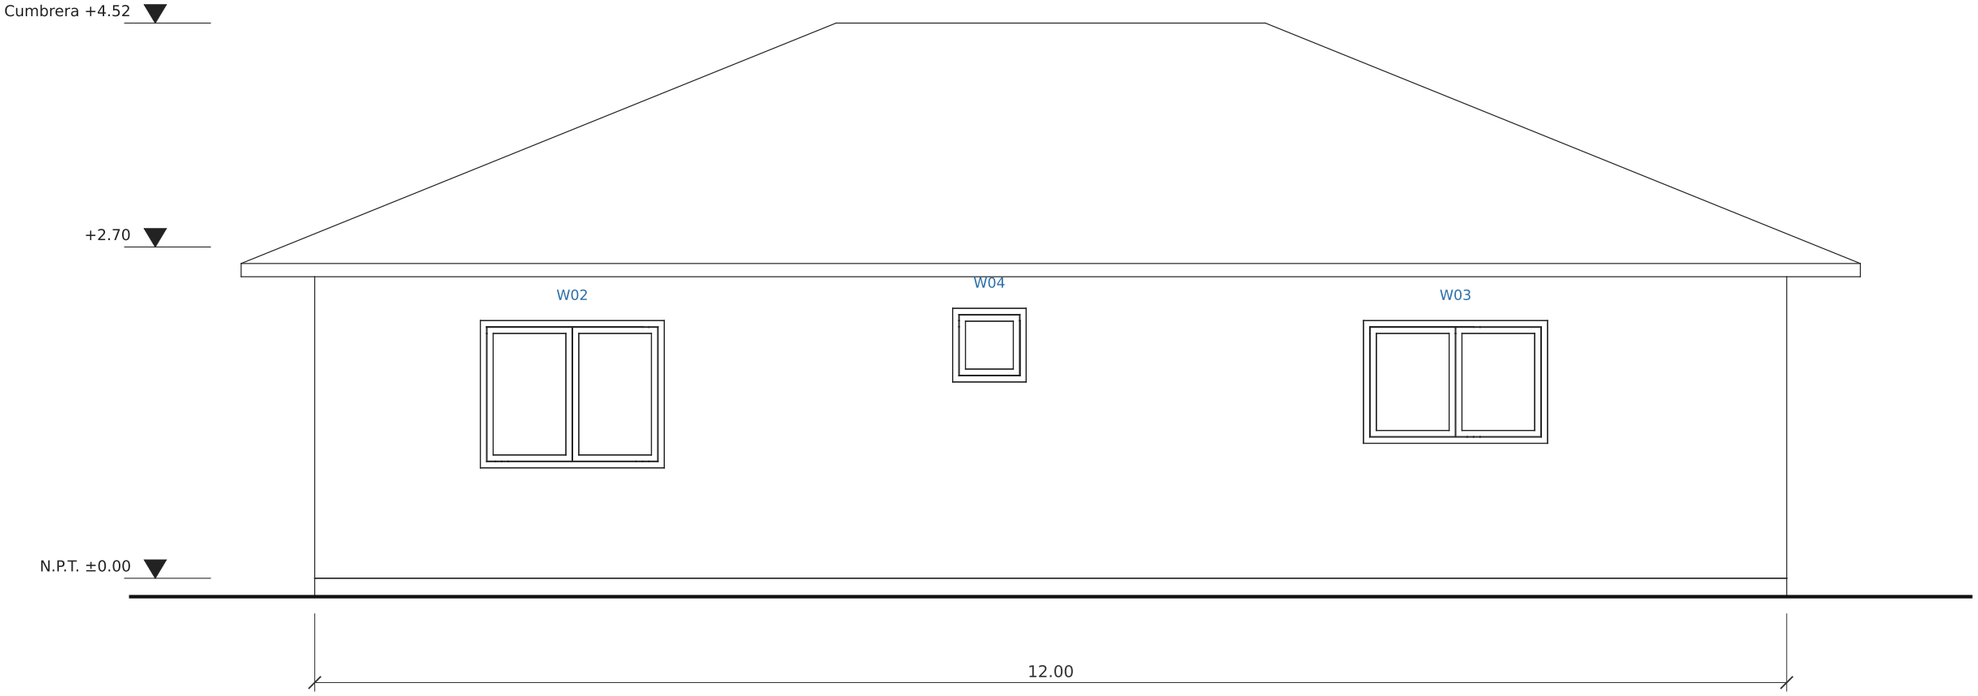

Fachada Norte

Escala 1:50

Casa de tres dormitorios

Fachadas

Escala 1:50 (hoja A3)

Niveles en metros

N.P.T.: nivel de piso terminado

Marcas de vanos según el cuadro de la hoja 1

Creado por Sebastian Mudarra

Hoja 2 de 3

Fachada Este

Escala 1:50

Fachada Oeste

Escala 1:50

Casa de tres dormitorios

Fachadas

Escala 1:50 (hoja A3)

Niveles en metros

N.P.T.: nivel de piso terminado

Marcas de vanos según el cuadro de la hoja 1

Creado por Sebastian Mudarra

Hoja 3 de 3