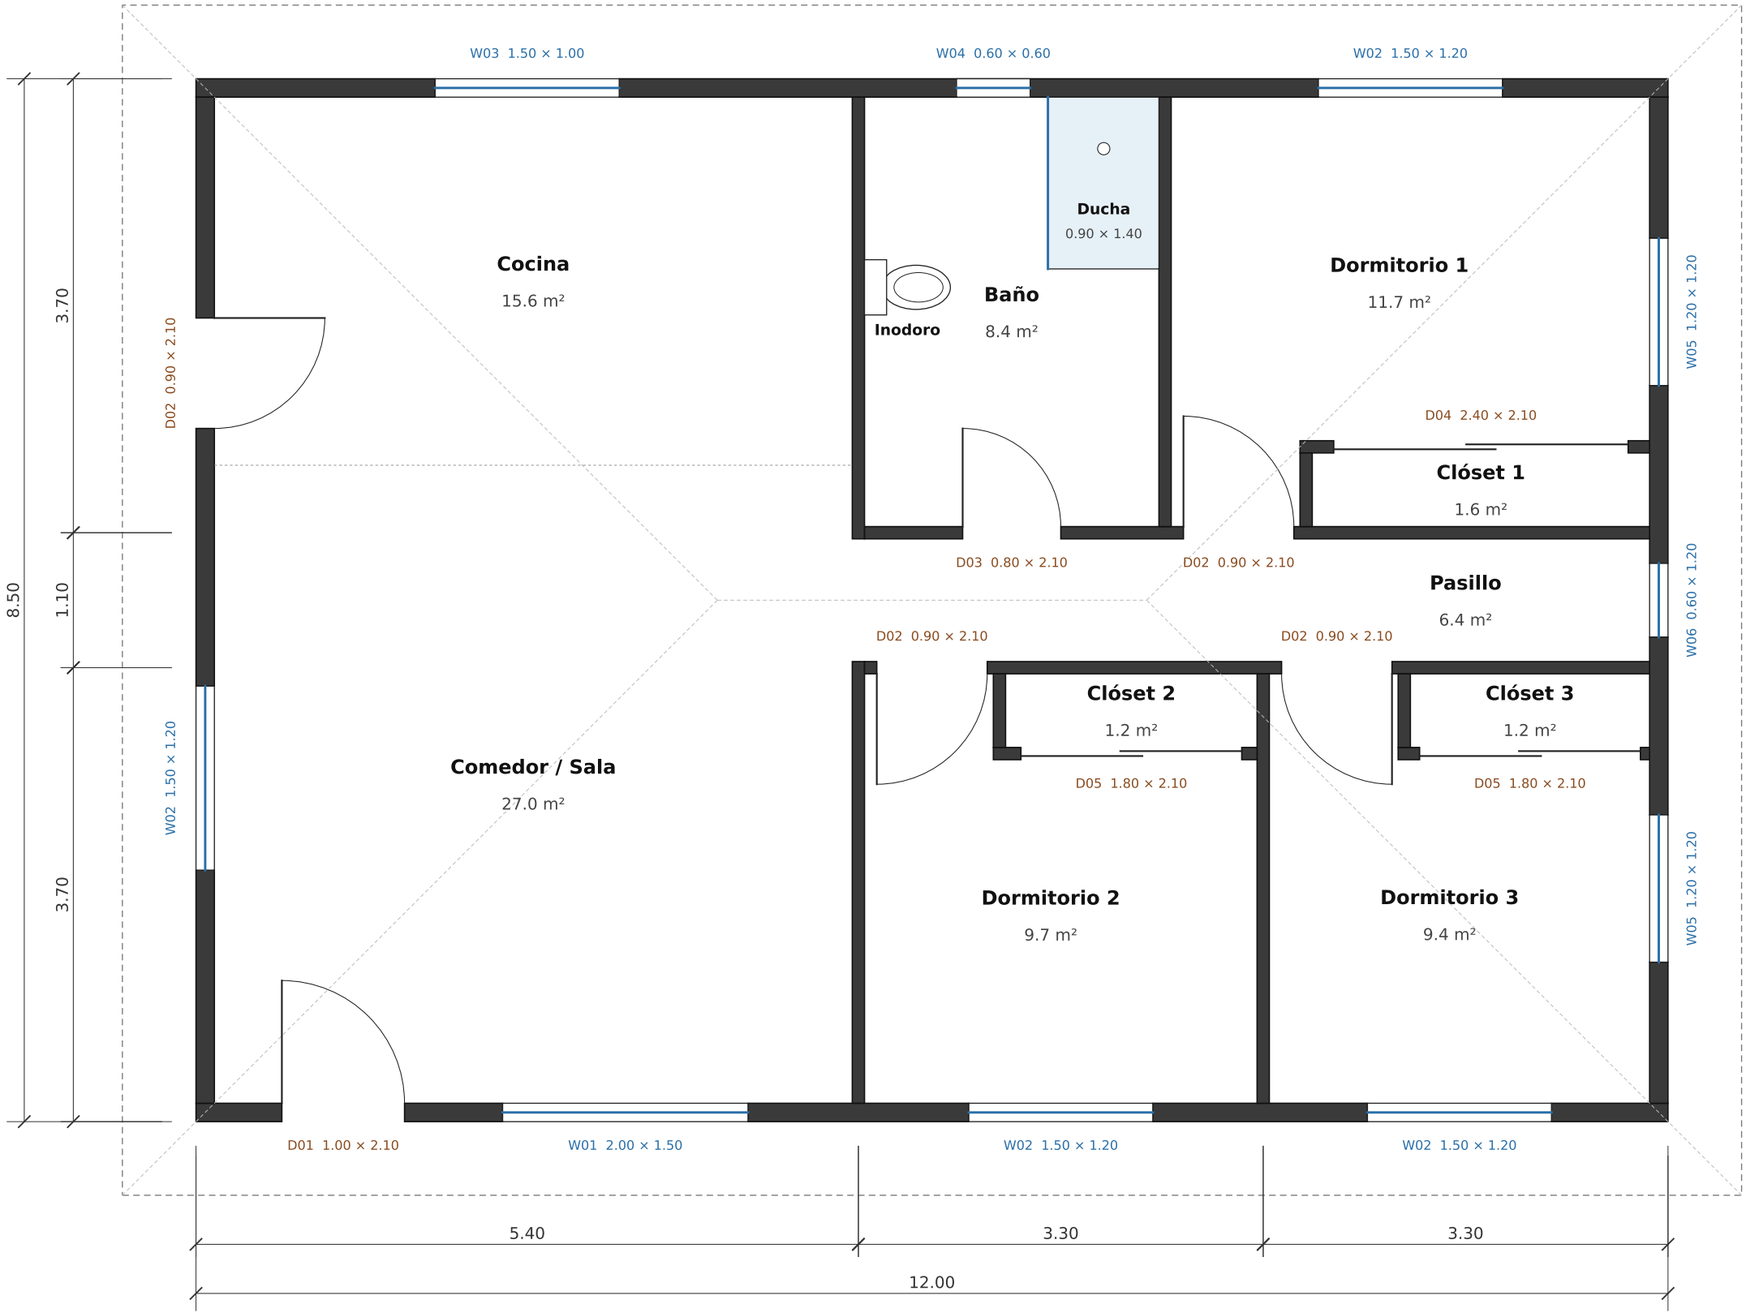


# Casa de tres dormitorios

Planta arquitectónica

Escala 1:50 (hoja A3)

Cotas en metros; vanos: ancho × alto

Área interior 92.3 m²

Área de construcción 102.0 m²

Línea discontinua: techo

Creado por Sebastian Mudarra

**Cuadro de puertas y ventanas (m)**

| Marca | Cant. | Ancho | Alto | Antepecho |
|---|---|---|---|---|
| W01 | 1 | 2.00 | 1.50 | 0.60 |
| W02 | 4 | 1.50 | 1.20 | 0.90 |
| W03 | 1 | 1.50 | 1.00 | 1.10 |
| W04 | 1 | 0.60 | 0.60 | 1.60 |
| W05 | 2 | 1.20 | 1.20 | 0.90 |
| W06 | 1 | 0.60 | 1.20 | 0.90 |
| D01 | 1 | 1.00 | 2.10 | – |
| D02 | 4 | 0.90 | 2.10 | – |
| D03 | 1 | 0.80 | 2.10 | – |
| D04 | 1 | 2.40 | 2.10 | – |
| D05 | 2 | 1.80 | 2.10 | – |